縮尺表記と平面図の図形に、約10%の不整合

TRC Eホール設備図 2025/12版 / JRRF公開スキャン / 比較日 2026-10-01

PDF内のベクトル座標を直接測定しました。「1/250」で図形をトレースすると、代表寸法を約10%大きく読み取ります。
右下のスケールバーは1/250と整合する一方、平面図の柱や横2mのグリッドは約1/227相当で描かれています。

確認箇所	図中の寸法表記	PDF図形を1/250で換算	結果
主要な横方向の寸法線	47.520 m	52.122 m	表記より約4.60 m大きい
天井グリッドの横ピッチ	2.000 m	2.201 m	約10.03%大きい
外側の柱の幅（例C11）	0.860 m	0.946 m	約10.02%大きい
外側の柱の奥行き（例C11）	1.050 m	1.155 m	約10.02%大きい
右下のスケールバー全長	10.000 m	10.0002 m	表記と一致

図形を読むための倍率

PDF自身のグリッドと柱寸法12件から求めた換算は 0.08015503 m/PDF point。実効縮尺は約1/227.21です。
1/250で作ったトレースを比較用に合わせる係数は約0.9088になります。これはPDF側の図形の補正で、スキャンを拡大縮小した結果ではありません。

寸法の数字はスキャンと近い

横の寸法表記47.520mに対し、モデルの代表的な壁間は47.527m。縦方向の表記40.380mに対して輪郭の最大スパンは40.434m、天井高4.000mに対して3.992mです。縦方向は比較端点が完全には一致しません。
PDFを縮尺表記やスケールバーから測って配置した場合は、「実際の会場が狭い」という経験の原因になり得ます。

局所的な描き方の差も残ります。例: グリッドの縦1.666mは、上記の倍率では約1.612mです。全ての線を一つの倍率で正確に直せるという意味ではありません。

図形の倍率を分けて、同じスキャンモデルに重ねる


TRC Eホール設備図 2025/12版 / JRRF公開スキャン / 比較日 2026-10-01

JRRF 会場 / 公式PDFとスキャン由来モデルの比較

スキャンの縮尺は固定。左: PDF表記どおり　右: PDF自身の寸法値で倍率を補正

1/250としてトレース

図形が約10%大きい / 位置は柱群の中心で合わせる

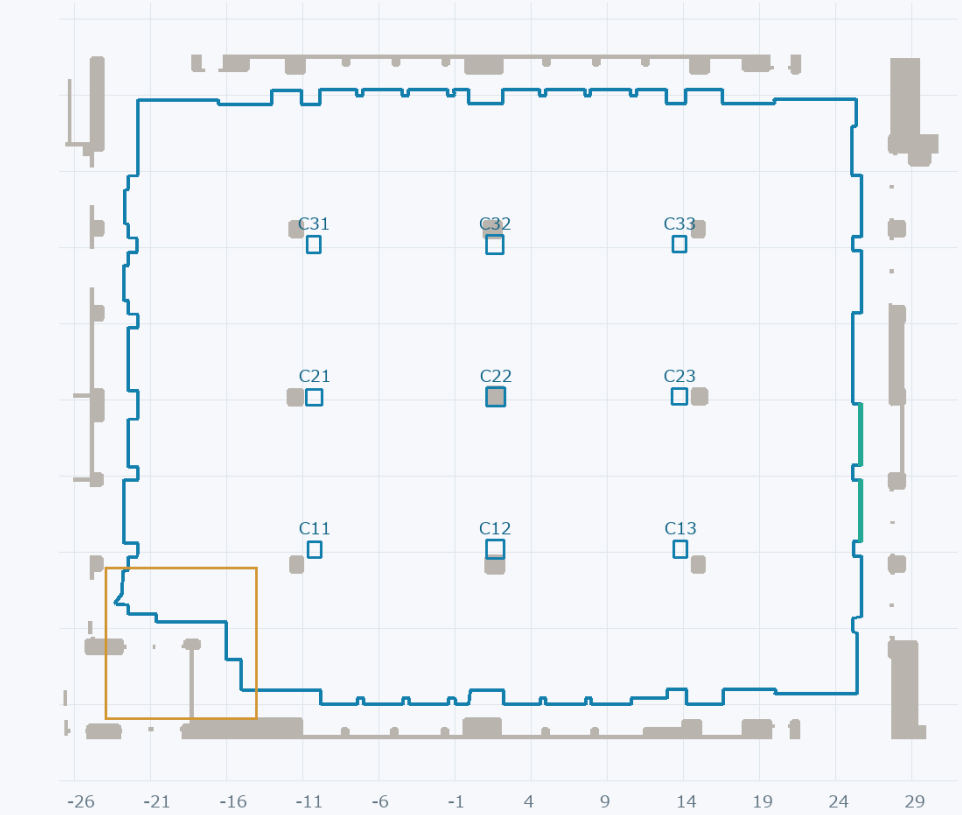


灰: 公式PDFの壁・柱図形　青: スキャン由来モデル　緑: 入口区画

橙の囲み: SW隅はモデル側の床輪郭も暫定。差をすべてPDF誤差にしない。

図中の寸法で補正して重ねる

倍率のみ補正、柱群で回転と平行移動を合わせる

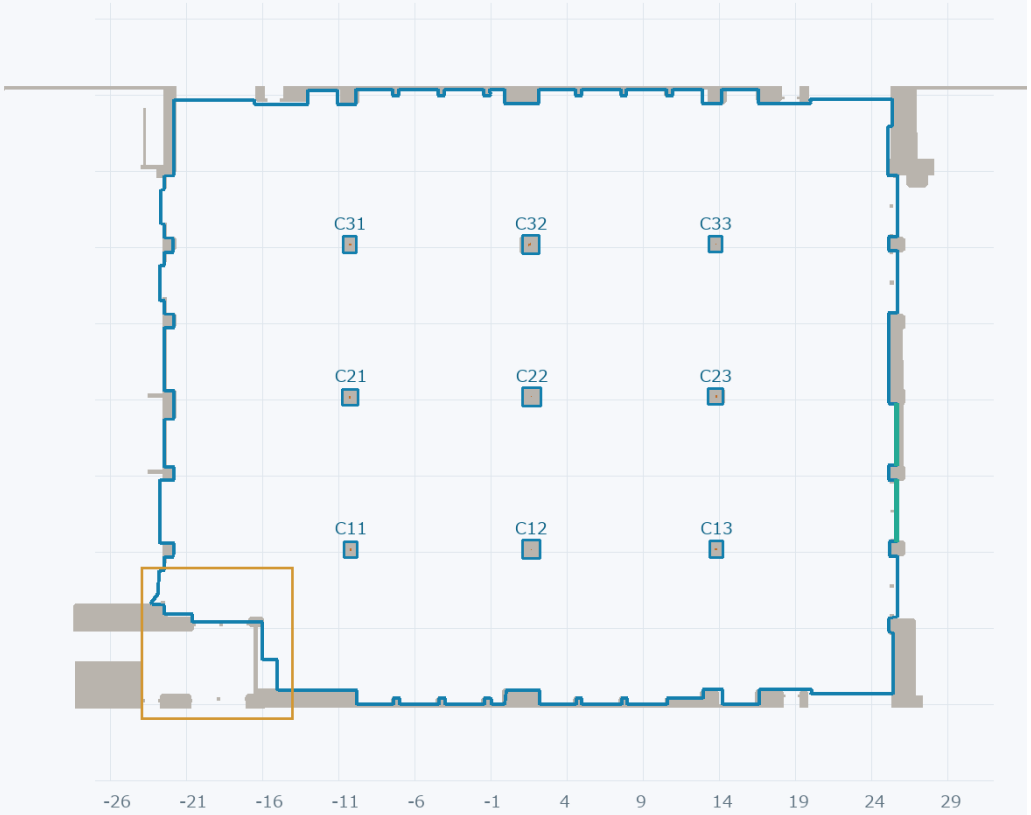

灰: 公式PDFの壁・柱図形　青: スキャン由来モデル　緑: 入口区画

橙の囲み: SW隅はモデル側の床輪郭も暫定。差をすべてPDF誤差にしない。

寸法値: 幅47.520m / スキャン代表幅47.527m　　柱の寸法差: 最大19mm

対象: TRC Eホール設備図 2025/12版 / JRRF公開スキャン。壁厚・ガラス・扉有効開口は未確定。

スキャンの倍率は1.0を維持。数値は公開メッシュと図面図形に対する比較。

柱寸法・位置の差と、比較の範囲

TRC Eホール設備図 2025/12版 / JRRF公開スキャン / 比較日 2026-10-01

柱サイズは図中の寸法値、柱位置は塗りつぶされた柱図形の中心と比較しています。位置合わせにはPDF自身の寸法から求めた倍率と、9本の柱を使った回転・平行移動のみを使用しました。

柱	PDF寸法 幅×奥行き [mm]	スキャンモデル [mm]	サイズ差 幅 / 奥行き [mm]	図形中心の位置差 [mm]
C11	860 × 1050	860.9 × 1069.5	+0.9 / +19.5	16.9
C12	1120 × 1190	1122.4 × 1195.9	+2.4 / +5.9	10.5
C13	860 × 1050	856.6 × 1059.8	-3.4 / +9.8	11.4
C21	990 × 1060	996.3 × 1065.1	+6.3 / +5.1	39.4
C22	1200 × 1200	1193.1 × 1203.3	-6.9 / +3.3	35.9
C23	990 × 1060	992.1 × 1056.3	+2.1 / -3.7	78.5
C31	860 × 1050	861.6 × 1055.3	+1.6 / +5.3	39.1
C32	1120 × 1190	1127.3 × 1199.2	+7.3 / +9.2	122.3
C33	860 × 1050	854.6 × 1056.1	-5.4 / +6.1	26.2

寸法値との差は最大約19.5mm。図形中心の位置差はRMS約54.5mm、最大約122.3mm（C32）。柱の図形や寸法補助線の配置にも差があり、この数値を柱そのものの施工誤差とは解釈しません。

面積とSW隅を「PDFの誤差」に含めない

公式サイトの面積1,984m²と、前回モデルの輪郭面積1854.5m²は定義がそろっていません。SW隅は高さ2.8mの上部断面から作った保守的な輪郭で、低い断面では外側にも床が見えます。隣接室の境界・低い天井の範囲も含めて暫定扱いとし、この面積差や局所差だけで公式図面の誤りを断定しません。

資料と再現方法

公式PDF: https://www.trc-event.jp/download/pdf/setsubi_e.pdf
公開スキャン: https://realsee.ai/VbOOJVjA 面積資料: https://www.trc-event.jp/hall/hall02.html
PDFは現在公開中のファイルとSHA-256が一致。文字はアウトライン化されているため寸法値を目視確認し、線の長さはPDFの座標から計算。比較用データは同梱JSON、柱ごとの数値はCSVに保存しています。